PROJETO ARQUITETÔNICO • EDIFICAÇÃO DE USO MISTO

IMPLANTAÇÃO, COBERTURA E QUADRO DE ÁREAS

IMPLANTAÇÃO • 1:150

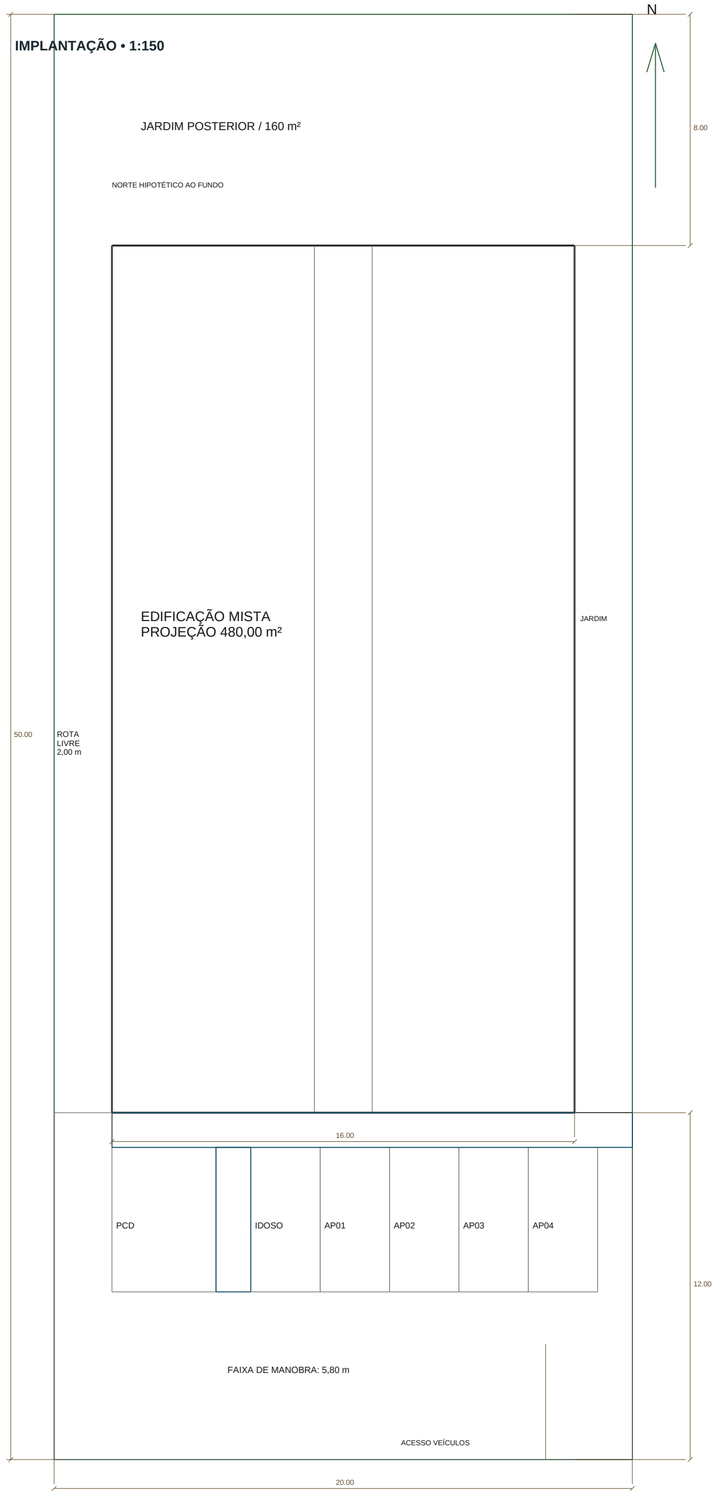

COBERTURA • 1:100

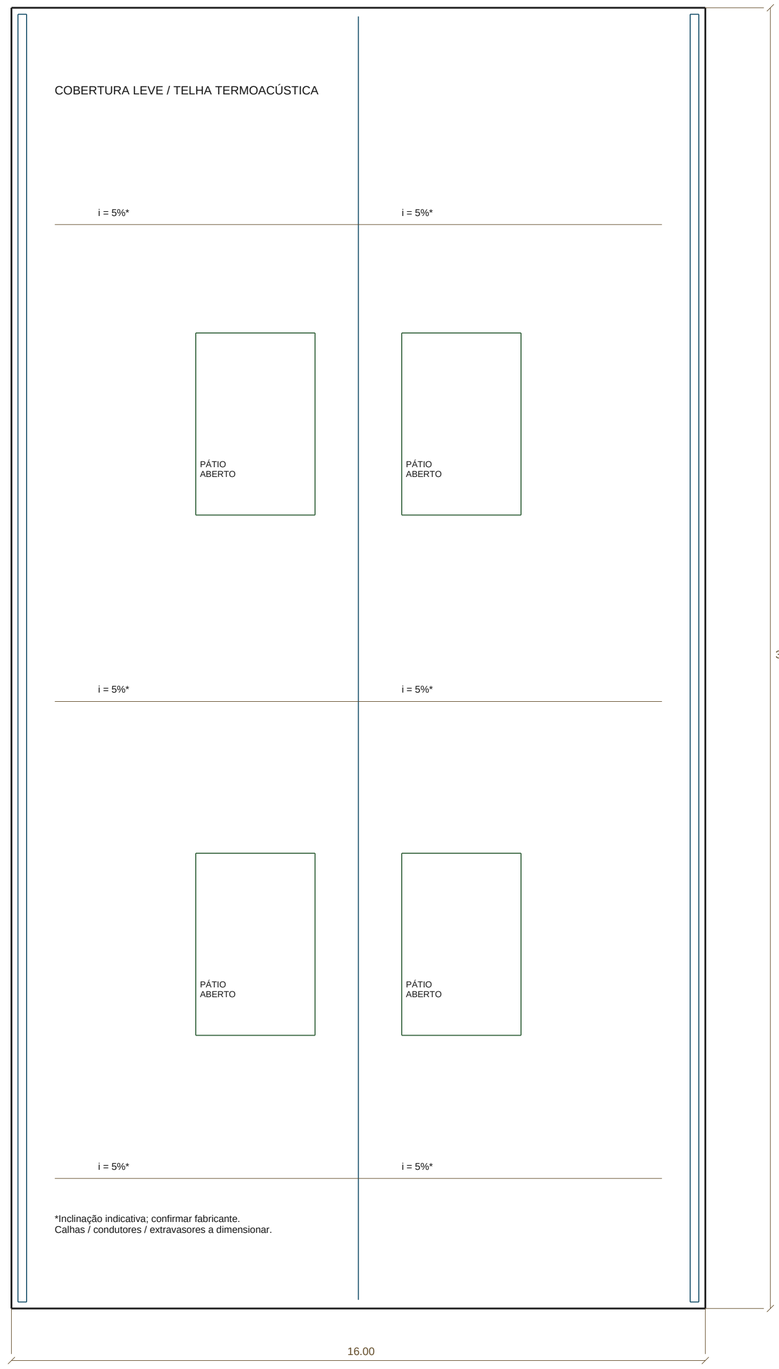

*Inclinação indicativa; confirmar fabricante.
Calhas / condutores / extravasores a dimensionar.

QUADRO DE ÁREAS BRUTAS

Terreno: 1.000,00 m²

Projeção: 480,00 m²

Térreo coberto: 480,00 m²

Superior coberto: 433,80 m²

TOTAL COBERTO: 913,80 m²

CONSTRUÍDA COM PÁTIOS: 960,00 m²

Pátios superiores descobertos: 46,20 m²

Lojas: 3 x 128,00 = 384,00 m²

Aptos: 4 x 72,45 = 289,80 m² cobertos

Cada unidade: + 11,55 m² de pátio

Áreas comuns: 240,00 m²

Livre no solo: 520,00 m²

Permeável proposta: 200,00 m² (20%)

Ocupação geométrica: 48%

CA com pátios: 0,96 / coberto: 0,9138

Áreas brutas incluem paredes e reservas. Pátios superiores não são permeabilidade do solo. Índices legais e cômputo municipal dependem de consulta de viabilidade.

HIPÓTESES: frente 12 m; fundo 8 m; laterais 2 m. Norte adotado ao fundo. Seis vagas propostas: 4 residenciais e 2 comerciais. Validar demanda da Tabela 05 e trajetórias. Não há endereço nem zoneamento fornecidos.

ALUNO: Icaro Gamarra Silva

RGM: 3322.527 | CURSO: Engenharia Civil

PROVA DE DESENHO TÉCNICO

PROJETO: 3 LOJAS + 4 APARTAMENTOS

PROFESSORA: Rafaella Scalon

LOCAL: Dourados - MS | Lote hipotético: 20 x 50 m

ENTREGA: 28/10/2026 | REVISÃO: 02

ESTUDO ACADÊMICO / NÃO EXECUTIVO

ESCALAS

1:150 / 1:100

UNIDADES: m / detalhes em cm indicados

01 / 08

A2 / 594 x 420