PROJETO ARQUITETÔNICO • EDIFICAÇÃO DE USO MISTO

PLANTA BAIXA COTADA E MOBILIADA • TÉRREO

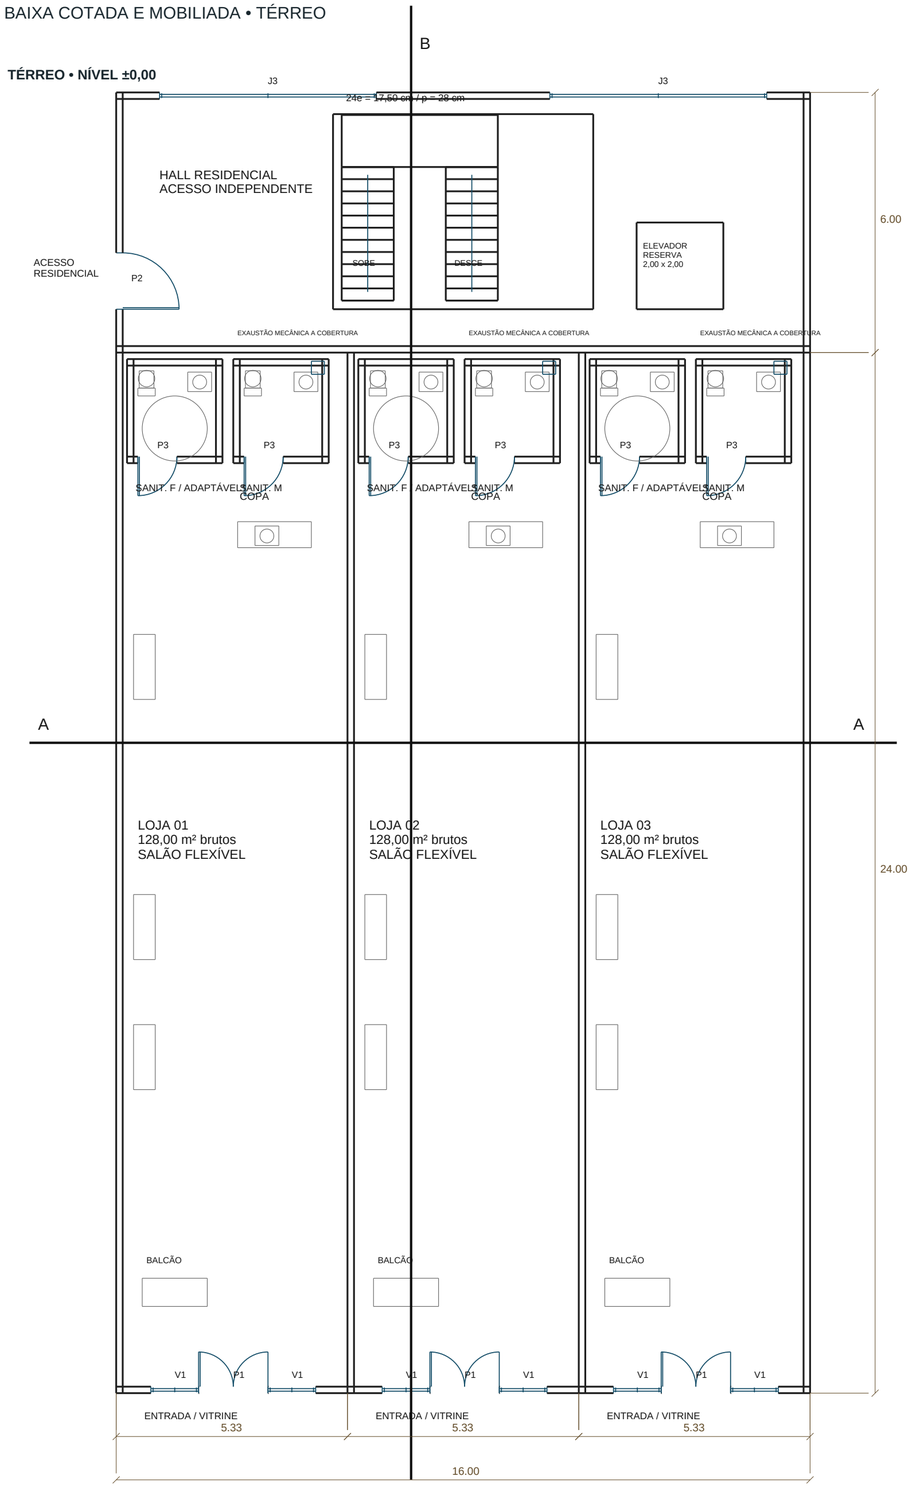

PROGRAMA COMERCIAL E CIRCULAÇÃO

Três lojas de 128,00 m² brutos, com entrada independente, salão flexível, copa e dois sanitários separados por sexo. Módulo de cada loja: 5,333 x 24,00 m. Faixa posterior: hall, escada, reserva de elevador e apoios. Acesso residencial pela lateral oeste, sem atravessar as lojas.

LEGENDA / ESQUADRIAS

P1: porta dupla comercial 1,60 x 2,70 m | qtd 3

P2: acesso residencial 1,30 x 2,40 m | qtd 1

P3: porta 0,90 x 2,10 m | qtd 14

P4: porta interna 0,80 x 2,10 m | qtd 16

V1: vitrine 1,10 x 2,70 m | qtd 6

J1: janela 2,20 x 1,50 m / peitoril 0,90 m | qtd 8

J2: cozinha 1,40 x 1,40 m / peitoril 1,10 m | qtd 4

J3: pano 5,00 x 1,20 m / peitoril variável | qtd 6

J4: banho 1,20 x 0,80 m / peitoril 1,50 m | qtd 4

J5: sala 3,60 x 1,90 m / peitoril 0,75 m | qtd 4

Portas com folha, batente e arco de abertura; janelas com marco, vidro e montante. Cotas em metros. Paredes externas/divisórias: 0,15 m indicativos. Não confundir dimensões modulares com vãos úteis.

*Sanitários comerciais: detalhe preliminar na prancha 07. A sobreposição do círculo de giro com peças deve ser avaliada conforme os critérios de aproximação e transferência da NBR 9050. Acessibilidade integral não está certificada.

ALUNO: Icaro Gamarra Silva

RGM: 3322.527 | CURSO: Engenharia Civil

PROVA DE DESENHO TÉCNICO

PROJETO: 3 LOJAS + 4 APARTAMENTOS

PROFESSORA: Rafaella Scalon

LOCAL: Dourados - MS | Lote hipotético: 20 x 50 m

ENTREGA: 28/10/2026 | REVISÃO: 02

ESTUDO ACADÊMICO / NÃO EXECUTIVO

ESCALAS

1:100

UNIDADES: m / detalhes em cm indicados

02 / 08

A2 / 594 x 420