PROJETO ARQUITETÔNICO • EDIFICAÇÃO DE USO MISTO

PLANTA BAIXA COTADA E MOBILIADA • SUPERIOR

SUPERIOR • NÍVEL +4,20

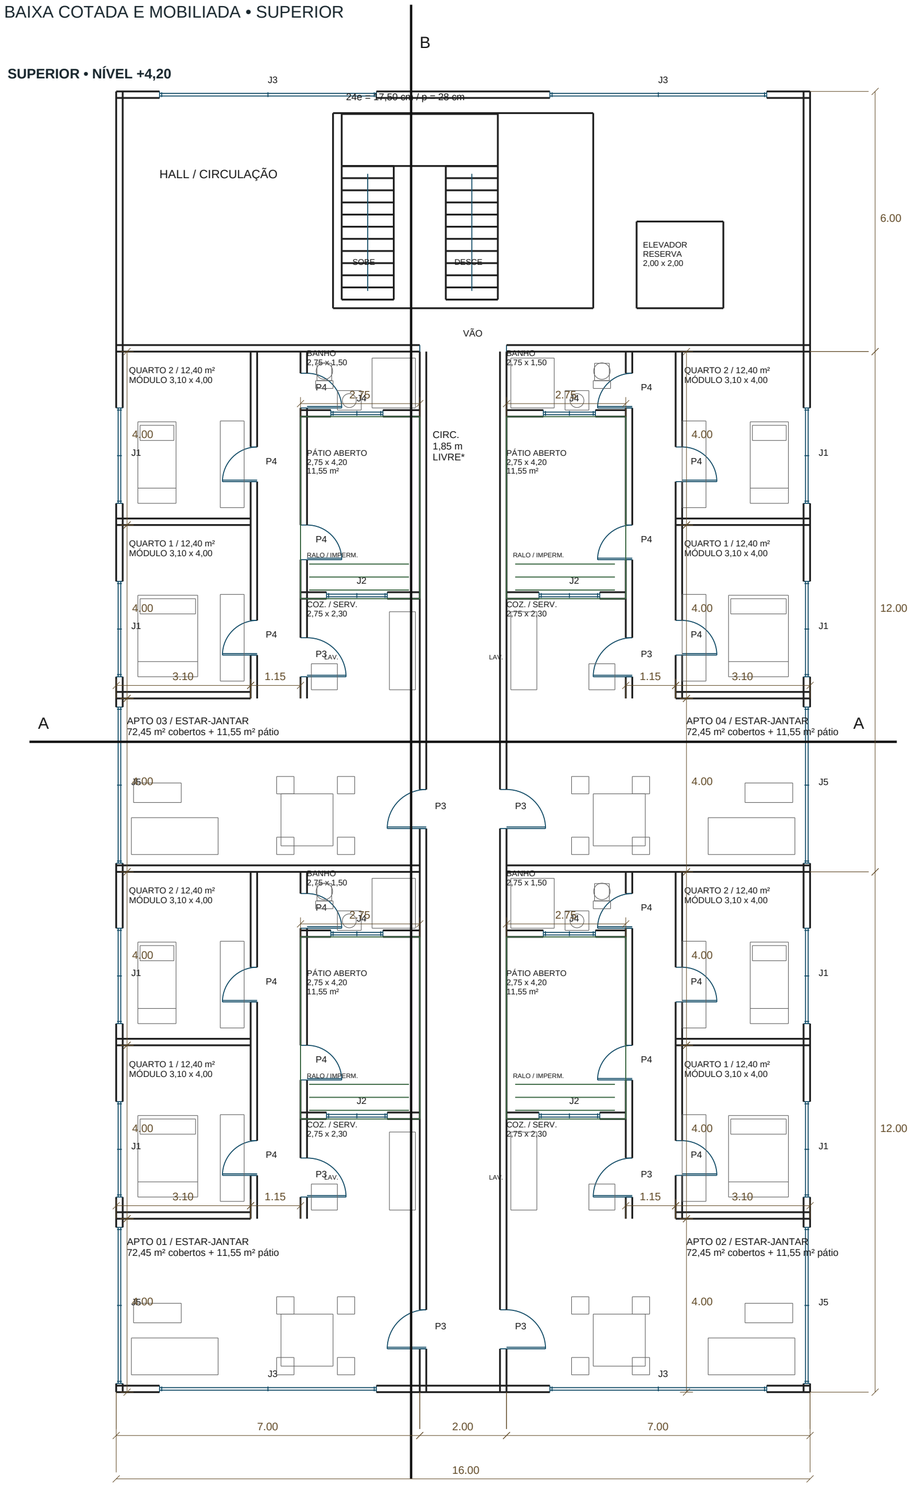

QUATRO APARTAMENTOS FAMILIARES

Cada unidade ocupa módulo de 7,00 x 12,00 m: 72,45 m² brutos cobertos e 11,55 m² de pátio descoberto. Estar/jantar, dois quartos, cozinha/serviço, banheiro e circulação. Quartos com janelas laterais; cozinha e banheiro voltados a pátio aberto à cobertura.

MÓDULOS DE AMBIENTES / POR UNIDADE

Estar/jantar: 7,00 x 4,00 = 28,00 m²

Quarto 1: 3,10 x 4,00 = 12,40 m²

Quarto 2: 3,10 x 4,00 = 12,40 m²

Cozinha/serviço: 2,75 x 2,30 = 6,325 m²

Banho: 2,75 x 1,50 = 4,125 m²

Circulação: 1,15 x 8,00 = 9,20 m²

Pátio aberto: 2,75 x 4,20 = 11,55 m²

Módulos não descontam paredes. Circulação coletiva nominal de 2,00 m; livre indicativa de 1,85 m entre faces. Portas de entrada com 0,90 m. Reserva de elevador não substitui projeto de acessibilidade e seleção de equipamento.

Pátios: dimensão livre proposta de 2,60 x 4,05 m (10,53 m²), comparada ao art. 27 do Código transcrito. Conferir razões de aberturas e confirmação legal. Prever impermeabilização, ralo e manutenção. A reformulação reduz a área coberta anterior para 913,80 m²; construída com pátios: 960 m².

ALUNO: Icaro Gamarra Silva

RGM: 3322.527 | CURSO: Engenharia Civil

PROVA DE DESENHO TÉCNICO

PROJETO: 3 LOJAS + 4 APARTAMENTOS

PROFESSORA: Rafaella Scalon

LOCAL: Dourados - MS | Lote hipotético: 20 x 50 m

ENTREGA: 28/10/2026 | REVISÃO: 02

ESTUDO ACADÊMICO / NÃO EXECUTIVO

ESCALAS

1:100

UNIDADES: m / detalhes em cm indicados

03 / 08

A2 / 594 x 420