

PROJETO ARQUITETÔNICO • EDIFICAÇÃO DE USO MISTO

IMPLANTAÇÃO, COBERTURA E QUADRO DE ÁREAS

IMPLANTAÇÃO • 1:150

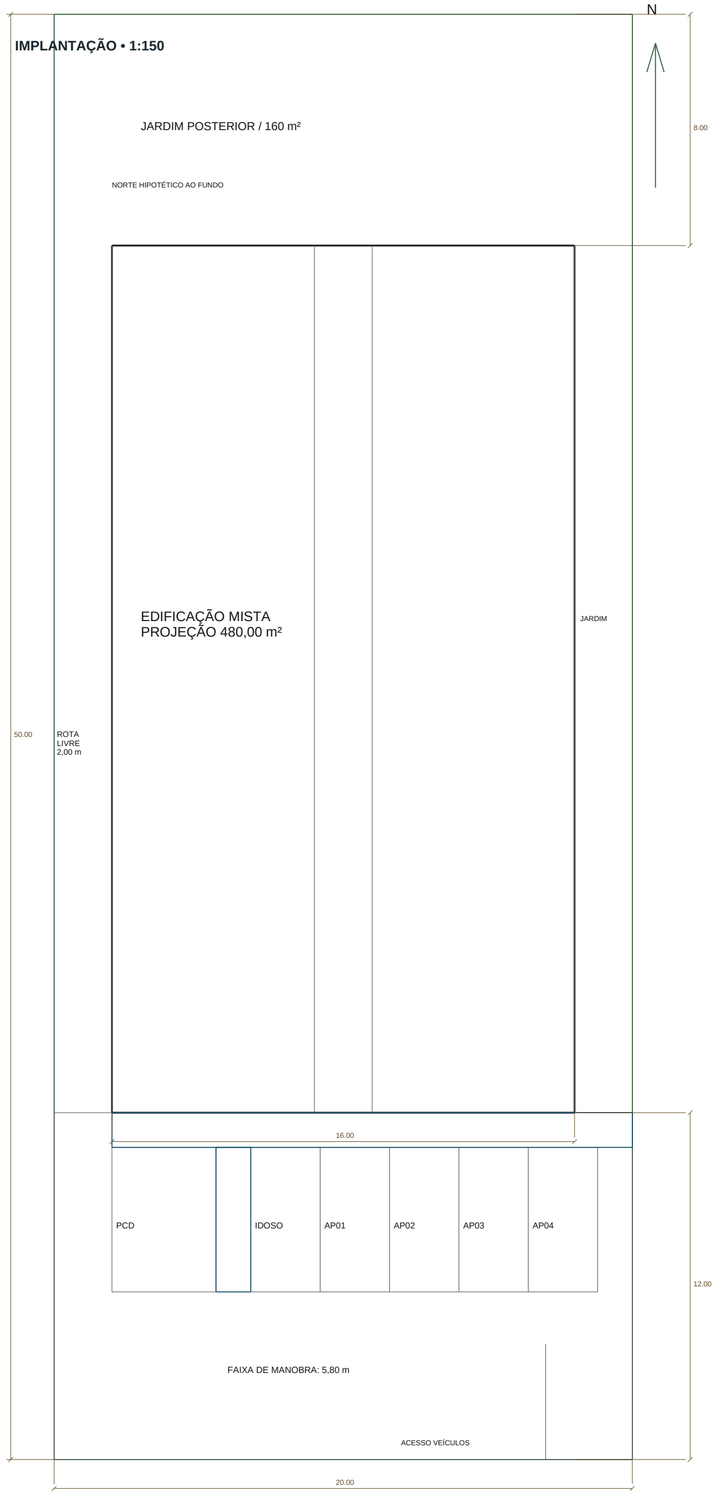

COBERTURA • 1:100

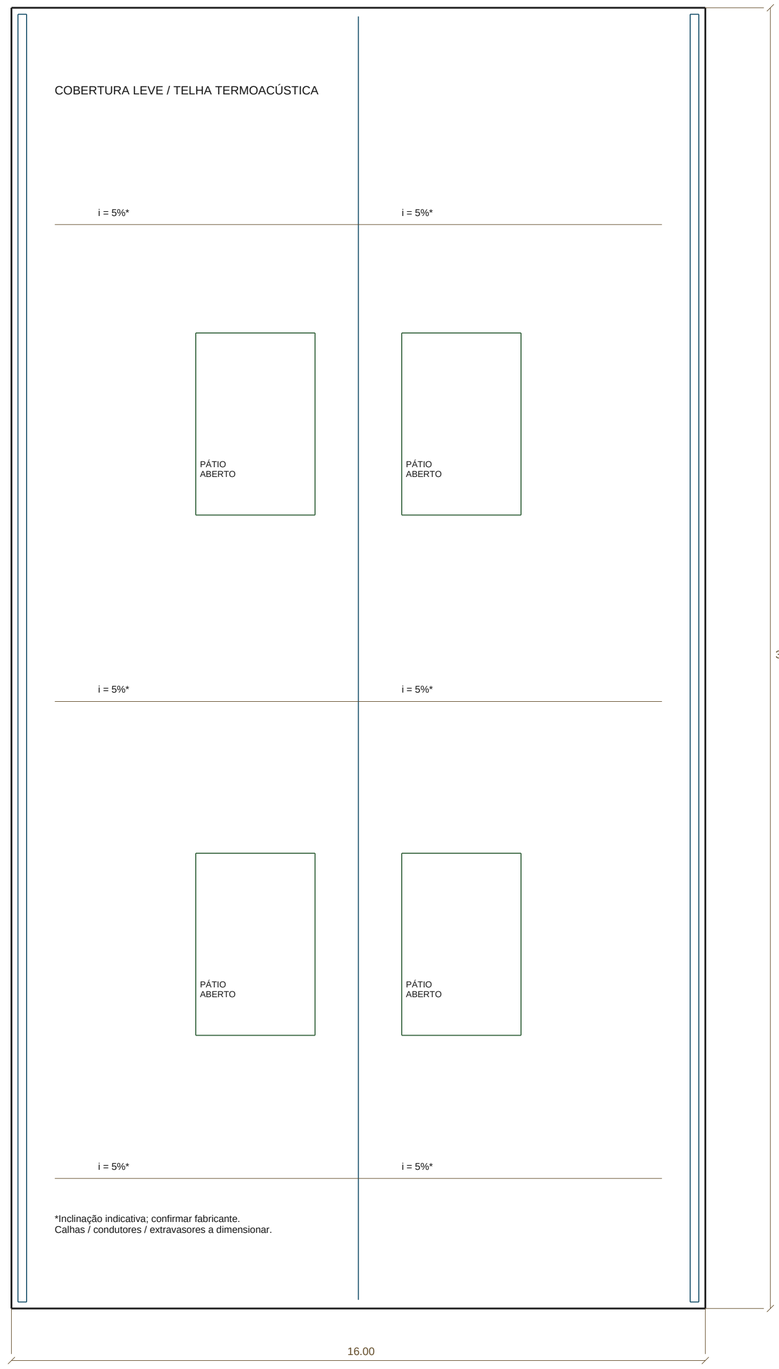

*Inclinação indicativa; confirmar fabricante.
Calhas / condutores / extravasores a dimensionar.

QUADRO DE ÁREAS BRUTAS

Terreno: 1.000,00 m²

Projeção: 480,00 m²

Térreo coberto: 480,00 m²

Superior coberto: 433,80 m²

TOTAL COBERTO: 913,80 m²

CONSTRUÍDA COM PÁTIOS: 960,00 m²

Pátios superiores descobertos: 46,20 m²

Lojas: 3 x 128,00 = 384,00 m²

Aptos: 4 x 72,45 = 289,80 m² cobertos

Cada unidade: + 11,55 m² de pátio

Áreas comuns: 240,00 m²

Livre no solo: 520,00 m²

Permeável proposta: 200,00 m² (20%)

Ocupação geométrica: 48%

CA com pátios: 0,96 / coberto: 0,9138

Áreas brutas incluem paredes e reservas. Pátios superiores não são permeabilidade do solo. Índices legais e cômputo municipal dependem de consulta de viabilidade.

HIPÓTESES: frente 12 m; fundo 8 m; laterais 2 m. Norte adotado ao fundo. Seis vagas propostas: 4 residenciais e 2 comerciais. Validar demanda da Tabela 05 e trajetórias. Não há endereço nem zoneamento fornecidos.

ALUNO: Icaro Gamarra Silva

RGM: 3322.527 | CURSO: Engenharia Civil

PROVA DE DESENHO TÉCNICO

PROJETO: 3 LOJAS + 4 APARTAMENTOS

PROFESSORA: Rafaella Scalon

LOCAL: Dourados - MS | Lote hipotético: 20 x 50 m

ENTREGA: 28/10/2026 | REVISÃO: 02

ESTUDO ACADÊMICO / NÃO EXECUTIVO

ESCALAS

1:150 / 1:100


UNIDADES: m / detalhes em cm indicados

01 / 08

A2 / 594 x 420

PROJETO ARQUITETÔNICO • EDIFICAÇÃO DE USO MISTO

PLANTA BAIXA COTADA E MOBILIADA • TÉRREO

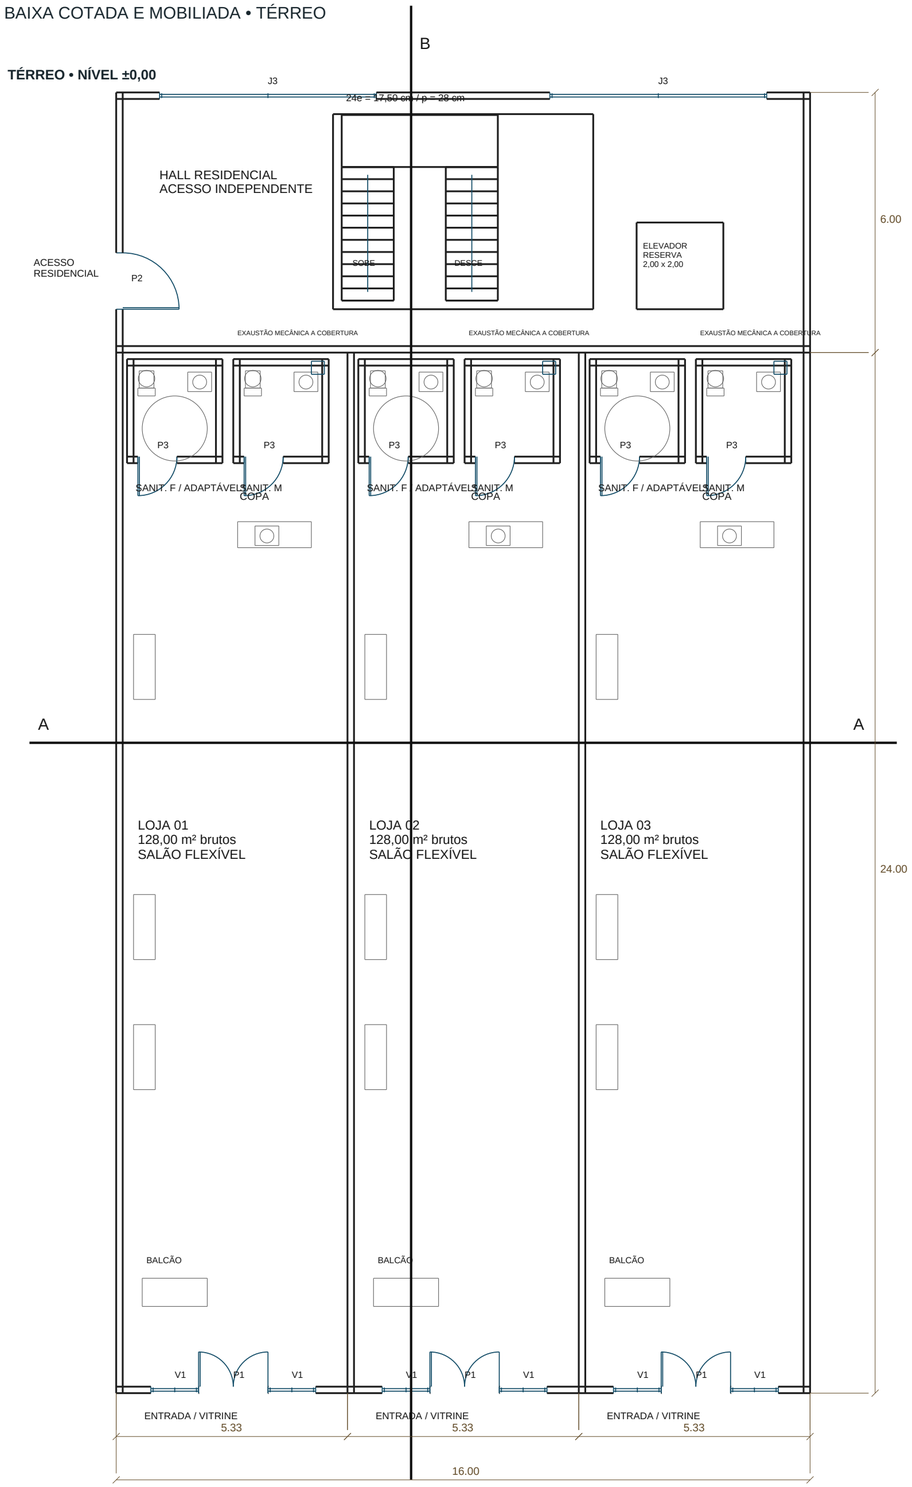

PROGRAMA COMERCIAL E CIRCULAÇÃO

Três lojas de 128,00 m² brutos, com entrada independente, salão flexível, copa e dois sanitários separados por sexo. Módulo de cada loja: 5,333 x 24,00 m. Faixa posterior: hall, escada, reserva de elevador e apoios. Acesso residencial pela lateral oeste, sem atravessar as lojas.

LEGENDA / ESQUADRIAS

P1: porta dupla comercial 1,60 x 2,70 m | qtd 3

P2: acesso residencial 1,30 x 2,40 m | qtd 1

P3: porta 0,90 x 2,10 m | qtd 14

P4: porta interna 0,80 x 2,10 m | qtd 16

V1: vitrine 1,10 x 2,70 m | qtd 6

J1: janela 2,20 x 1,50 m / peitoril 0,90 m | qtd 8

J2: cozinha 1,40 x 1,40 m / peitoril 1,10 m | qtd 4

J3: pano 5,00 x 1,20 m / peitoril variável | qtd 6

J4: banho 1,20 x 0,80 m / peitoril 1,50 m | qtd 4

J5: sala 3,60 x 1,90 m / peitoril 0,75 m | qtd 4

Portas com folha, batente e arco de abertura; janelas com marco, vidro e montante. Cotas em metros. Paredes externas/divisórias: 0,15 m indicativos. Não confundir dimensões modulares com vãos úteis.

*Sanitários comerciais: detalhe preliminar na prancha 07. A sobreposição do círculo de giro com peças deve ser avaliada conforme os critérios de aproximação e transferência da NBR 9050. Acessibilidade integral não está certificada.

ALUNO: Icaro Gamarra Silva

RGM: 3322.527 | CURSO: Engenharia Civil

PROVA DE DESENHO TÉCNICO

PROJETO: 3 LOJAS + 4 APARTAMENTOS

PROFESSORA: Rafaella Scalon

LOCAL: Dourados - MS | Lote hipotético: 20 x 50 m

ENTREGA: 28/10/2026 | REVISÃO: 02

ESTUDO ACADÊMICO / NÃO EXECUTIVO

ESCALAS


1:100

UNIDADES: m / detalhes em cm indicados

PROJETO ARQUITETÔNICO • EDIFICAÇÃO DE USO MISTO

PLANTA BAIXA COTADA E MOBILIADA • SUPERIOR

SUPERIOR • NÍVEL +4,20

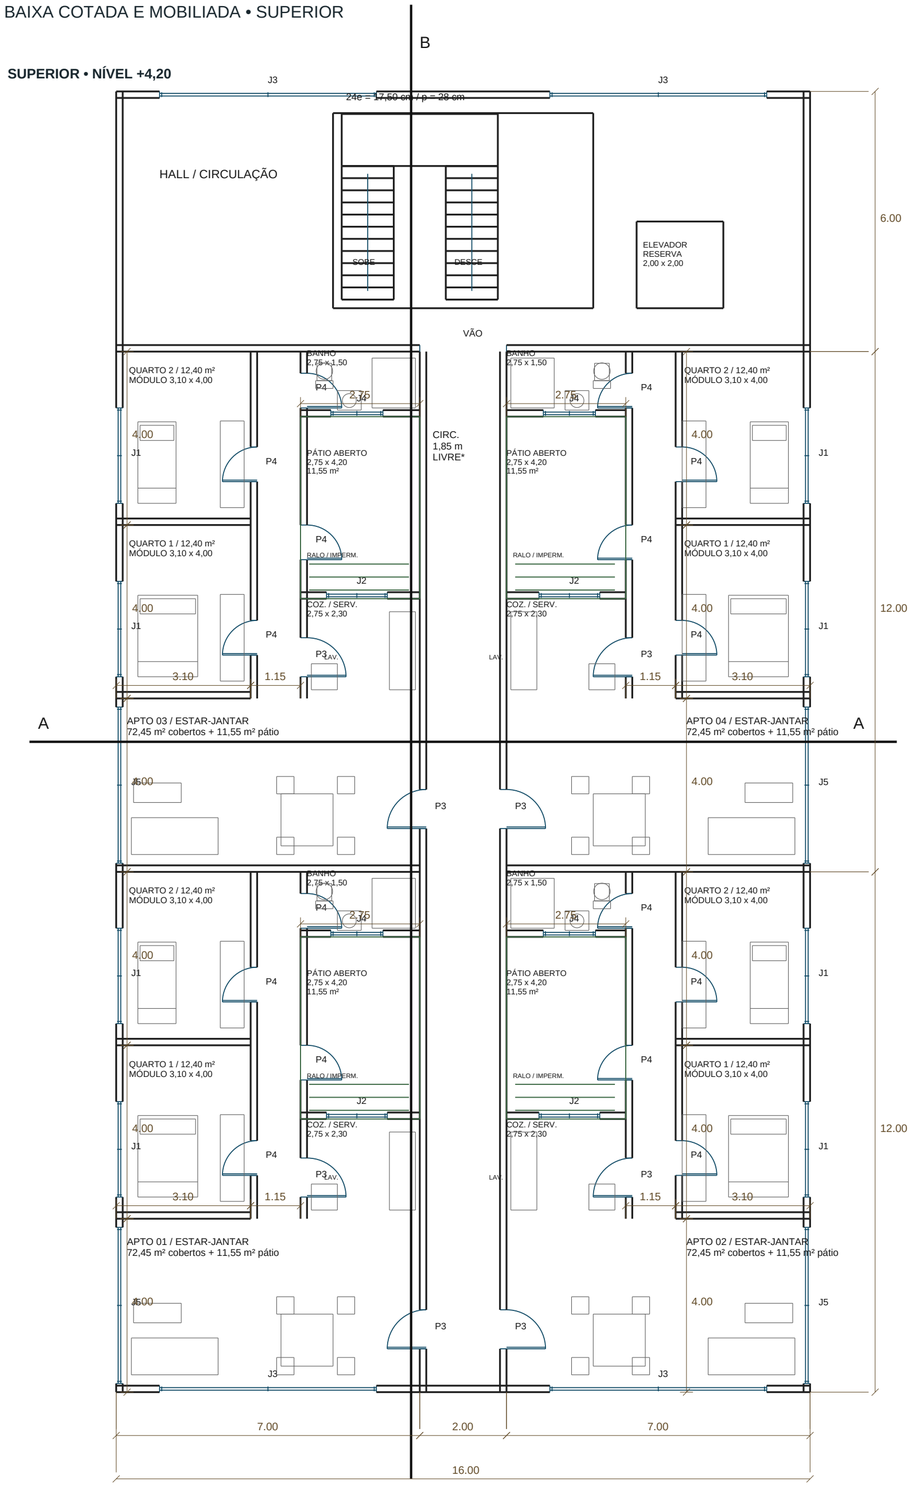

QUATRO APARTAMENTOS FAMILIARES

Cada unidade ocupa módulo de 7,00 x 12,00 m: 72,45 m² brutos cobertos e 11,55 m² de pátio descoberto. Estar/jantar, dois quartos, cozinha/serviço, banheiro e circulação. Quartos com janelas laterais; cozinha e banheiro voltados a pátio aberto à cobertura.

MÓDULOS DE AMBIENTES / POR UNIDADE

Estar/jantar: 7,00 x 4,00 = 28,00 m²

Quarto 1: 3,10 x 4,00 = 12,40 m²

Quarto 2: 3,10 x 4,00 = 12,40 m²

Cozinha/serviço: 2,75 x 2,30 = 6,325 m²

Banho: 2,75 x 1,50 = 4,125 m²

Circulação: 1,15 x 8,00 = 9,20 m²

Pátio aberto: 2,75 x 4,20 = 11,55 m²

Módulos não descontam paredes. Circulação coletiva nominal de 2,00 m; livre indicativa de 1,85 m entre faces. Portas de entrada com 0,90 m. Reserva de elevador não substitui projeto de acessibilidade e seleção de equipamento.

Pátios: dimensão livre proposta de 2,60 x 4,05 m (10,53 m²), comparada ao art. 27 do Código transcrito. Conferir razões de aberturas e confirmação legal. Prever impermeabilização, ralo e manutenção. A reformulação reduz a área coberta anterior para 913,80 m²; construída com pátios: 960 m².

ALUNO: Icaro Gamarra Silva

RGM: 3322.527 | CURSO: Engenharia Civil

PROVA DE DESENHO TÉCNICO

PROJETO: 3 LOJAS + 4 APARTAMENTOS

PROFESSORA: Rafaella Scalon

LOCAL: Dourados - MS | Lote hipotético: 20 x 50 m

ENTREGA: 28/10/2026 | REVISÃO: 02

ESTUDO ACADÊMICO / NÃO EXECUTIVO

ESCALAS

1:100

UNIDADES: m / detalhes em cm indicados


03 / 08

A2 / 594 x 420

PROJETO ARQUITETÔNICO • EDIFICAÇÃO DE USO MISTO

CORTES LONGITUDINAL B–B E TRANSVERSAL A–A


B–B • LONGITUDINAL / X=8,80 m

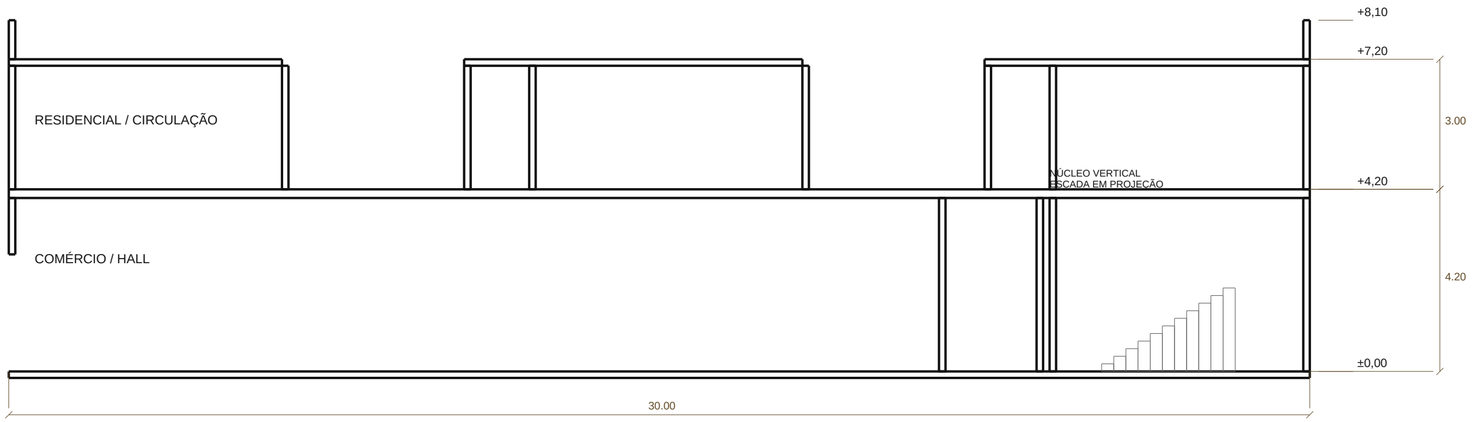

NÍVEIS: térreo ±0,00; superior +4,20; cobertura +7,20; platibanda +8,10. Laje intermediária 20 cm; cobertura 15 cm. Pés-direitos antes de forros: 4,00 m e 2,85 m.

As seções usam a posição real das paredes e aberturas do modelo. A escada aparece em projeção no corte B, pois o plano passa entre os lances. Ver desenvolvimento na prancha 06.

A–A • TRANSVERSAL / Y=27,00 m

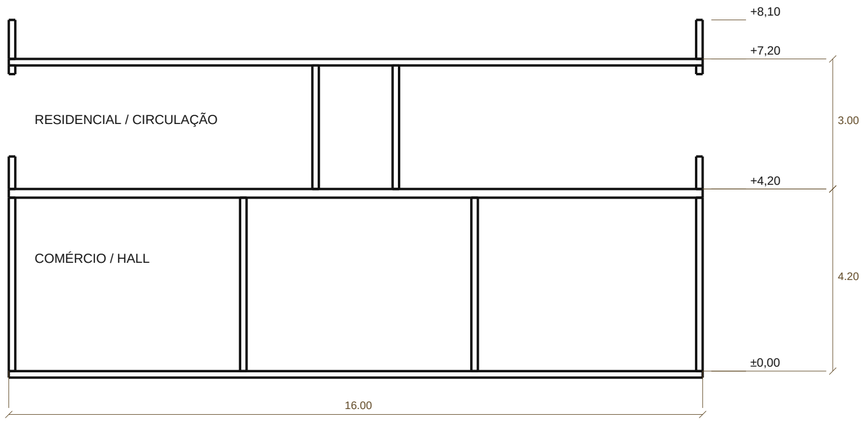

SISTEMA CONSTRUTIVO PROPOSTO: estrutura de concreto armado a dimensionar, alvenaria de vedação e cobertura leve termoacústica protegida por platibanda. Não foram dimensionados pilares, vigas, fundações ou armações.

ALUNO: Icaro Gamarra Silva

RGM: 3322.527 | CURSO: Engenharia Civil

PROVA DE DESENHO TÉCNICO

PROJETO: 3 LOJAS + 4 APARTAMENTOS

PROFESSORA: Rafaella Scalon

LOCAL: Dourados - MS | Lote hipotético: 20 x 50 m

ENTREGA: 28/10/2026 | REVISÃO: 02

ESTUDO ACADÊMICO / NÃO EXECUTIVO

ESCALAS

1:100

UNIDADES: m / detalhes em cm indicados


04 / 08

A2 / 594 x 420


PROJETO ARQUITETÔNICO • EDIFICAÇÃO DE USO MISTO

FACHADAS FRONTAL, POSTERIOR, OESTE E LESTE


FRONTAL / TESTADA

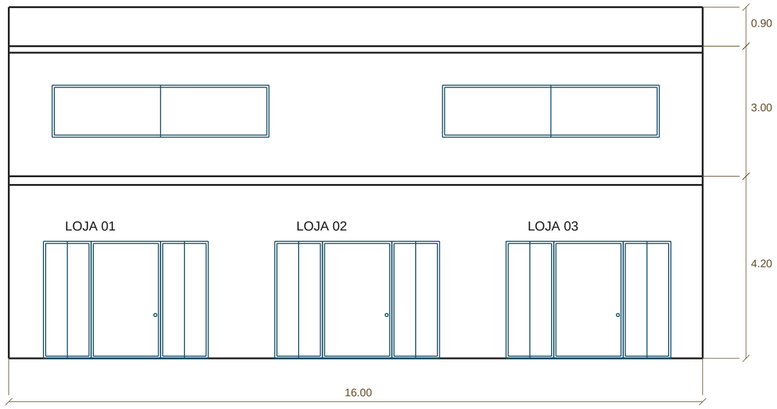


POSTERIOR

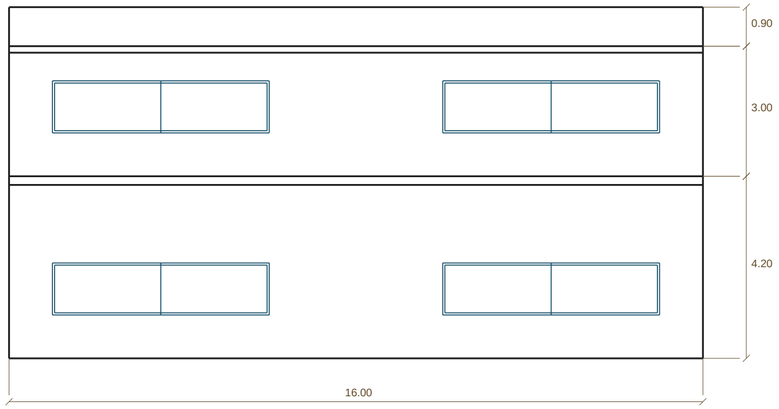

LATERAL OESTE / ACESSO RESIDENCIAL

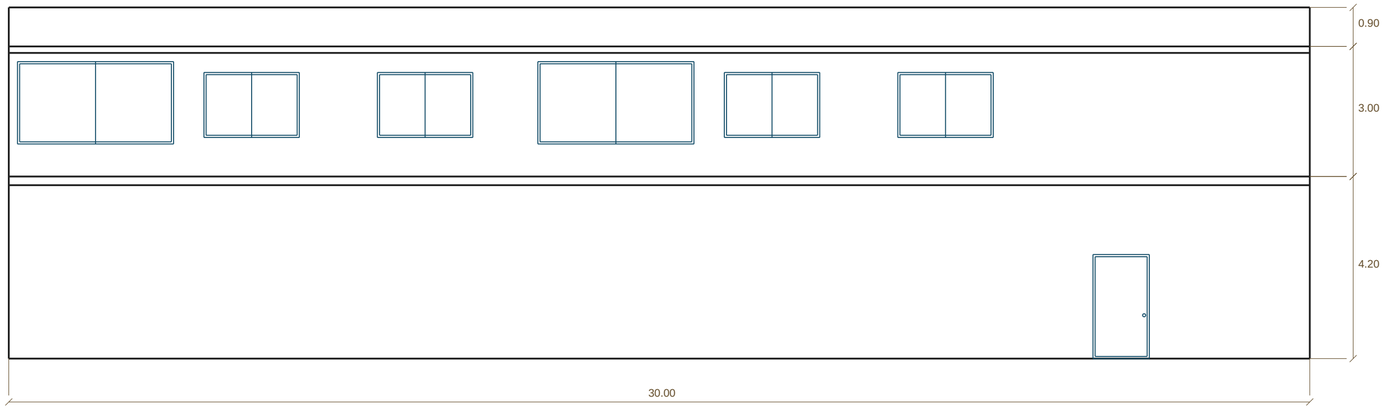

LATERAL LESTE

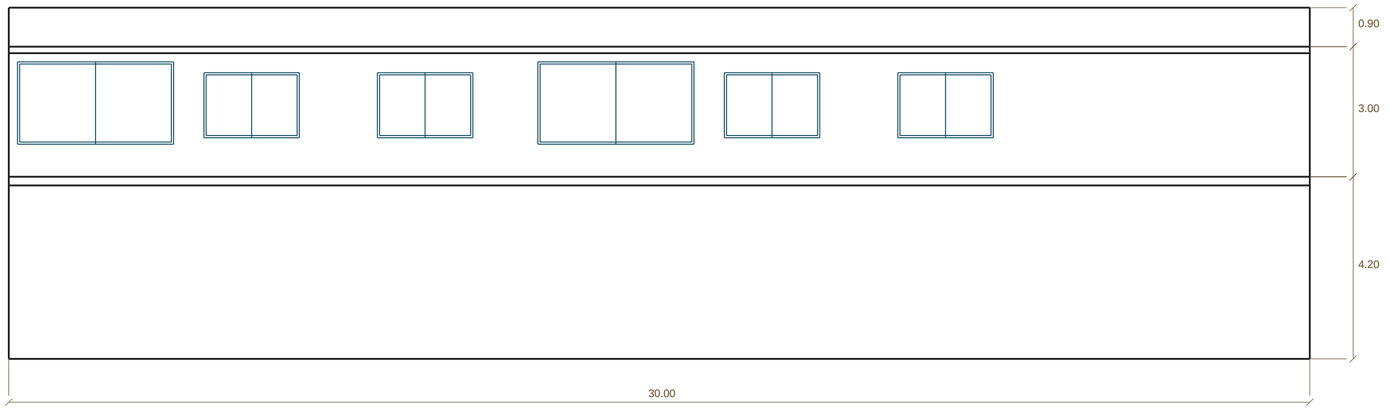

ACABAMENTOS: pintura clara, caixilhos em alumínio grafite, vidros a especificar, portas comerciais com painéis laterais envidraçados. Prever sombreamento conforme orientação real.

As aberturas destas fachadas são obtidas da mesma geometria das plantas e do modelo 3D. Alturas e peitoris constam na legenda de esquadrias.

ALUNO: Icaro Gamarra Silva

RGM: 3322.527 | CURSO: Engenharia Civil

PROVA DE DESENHO TÉCNICO

PROJETO: 3 LOJAS + 4 APARTAMENTOS

PROFESSORA: Rafaella Scalon

LOCAL: Dourados - MS | Lote hipotético: 20 x 50 m

ENTREGA: 28/10/2026 | REVISÃO: 02

ESTUDO ACADÊMICO / NÃO EXECUTIVO

ESCALAS

1:100

UNIDADES: m / detalhes em cm indicados


05 / 08

A2 / 594 x 420

PROJETO ARQUITETÔNICO • EDIFICAÇÃO DE USO MISTO

DETALHES DE ESCADA, PORTA, JANELA E IMPERMEABILIZAÇÃO

ESCADA EM U • 1:25

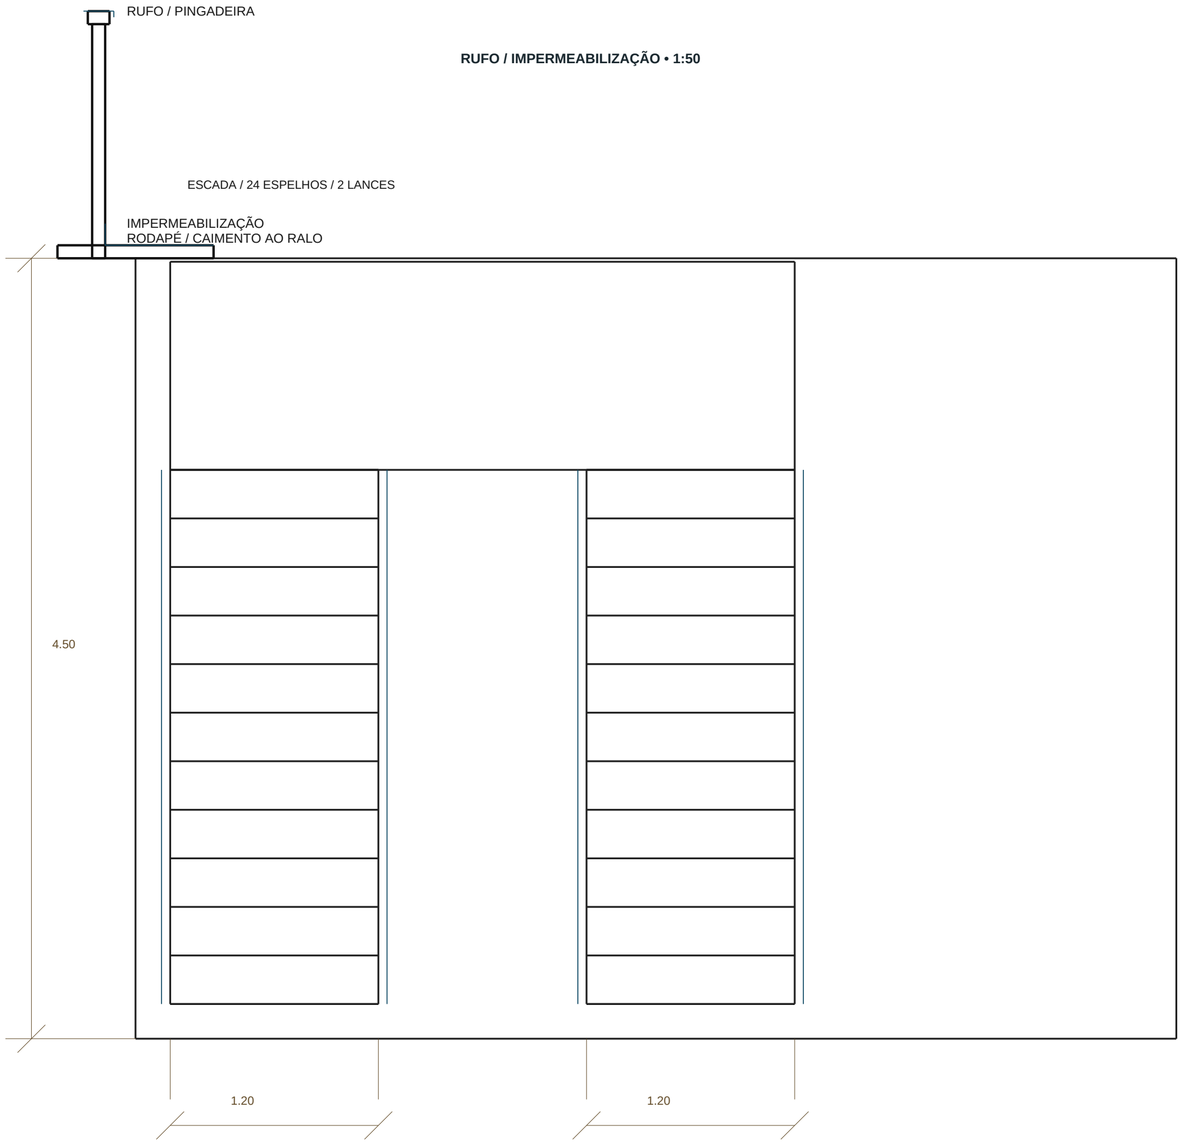


RUFO / IMPERMEABILIZAÇÃO • 1:50


Escada: 24 espelhos de 17,50 cm; piso 28 cm; 2e+p = 63,00 cm. Lances de 1,20 m e patamar de 1,20 m. Corrimãos em duas alturas e guarda-corpo a detalhar conforme norma aplicável. Verificar altura livre e exigência de escada protegida.

PORTA P3 • 1:20

VISTA / BATENTE E FOLHA

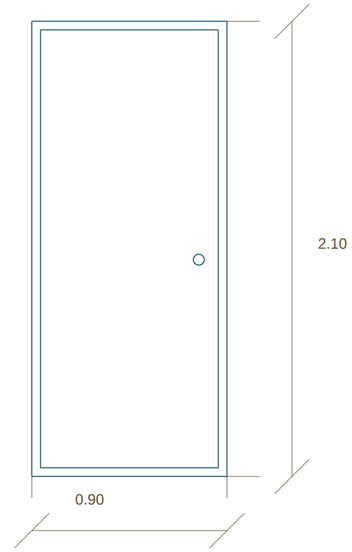



PLANTA / PORTA P3

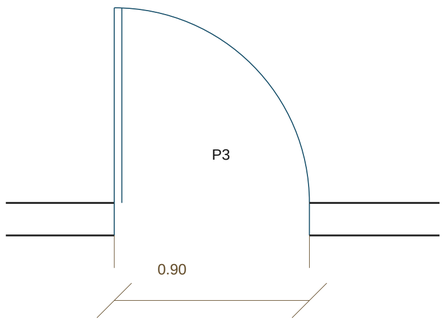

JANELA J1 • 1:25

J1 / ABRIR / ÁREA LIVRE >=70%

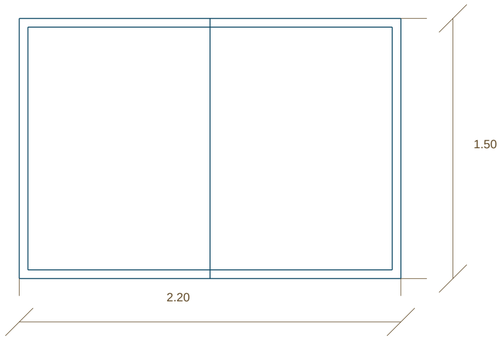

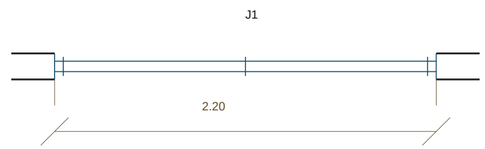

Detalhes de batentes, folhas, marcos e peitoril. Cotas gerais em metros. Rufo e impermeabilização são esquemas construtivos, sem especificação executiva.

ALUNO: Icaro Gamarra Silva

RGM: 3322.527 | CURSO: Engenharia Civil

PROVA DE DESENHO TÉCNICO

PROJETO: 3 LOJAS + 4 APARTAMENTOS

PROFESSORA: Rafaella Scalon

LOCAL: Dourados - MS | Lote hipotético: 20 x 50 m

ENTREGA: 28/10/2026 | REVISÃO: 02

ESTUDO ACADÊMICO / NÃO EXECUTIVO

ESCALAS

1:25 / 1:20 / 1:50

UNIDADES: m / detalhes em cm indicados


06 / 08

A2 / 594 x 420

PROJETO ARQUITETÔNICO • EDIFICAÇÃO DE USO MISTO


APARTAMENTO AMPLIADO E SANITÁRIO COMERCIAL

APARTAMENTO 01 • 1:50

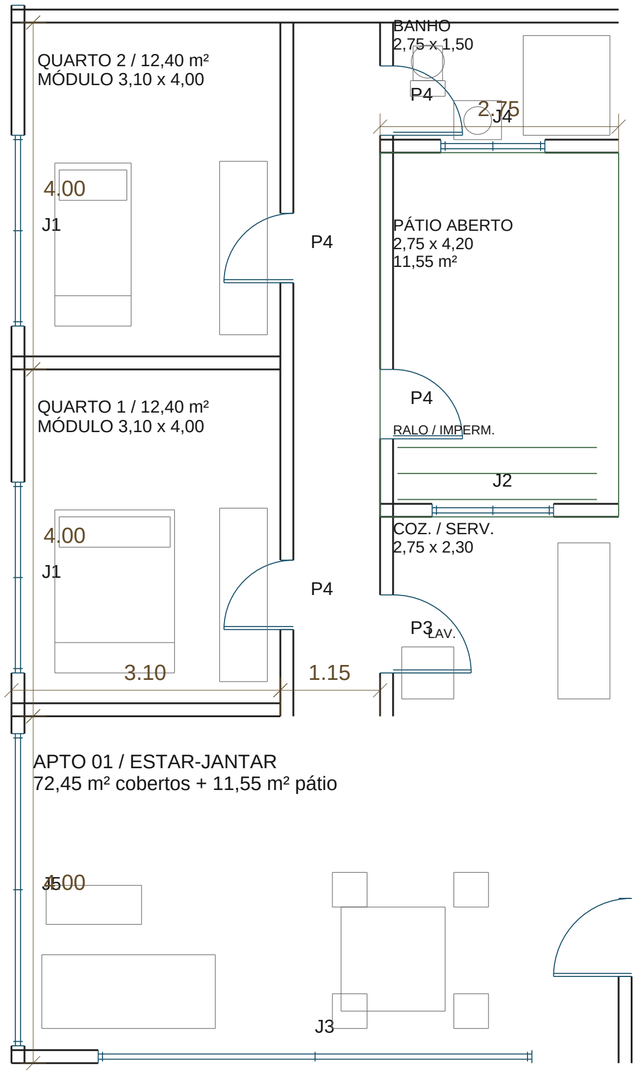

SANITÁRIO COMERCIAL • 1:25

SANITÁRIO / ARRANJO PRELIMINAR
Círculo de giro e barras indicativas.
Conferir transferências livres na etapa legal.

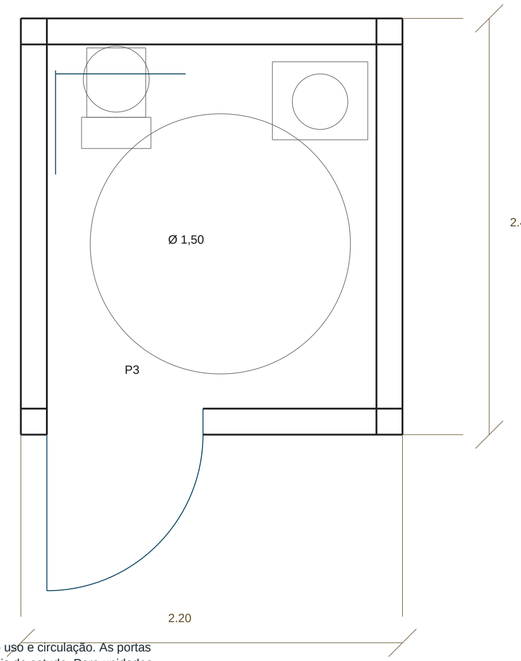

A disposição de mobiliário permite leitura do uso e circulação. As portas internas com 0,80 m são dimensões nominais de estudo. Para unidades acessíveis/adaptáveis, conferir vãos livres, áreas de manobra, aproximações, soleiras e instalações. O sanitário comercial tem porta abrindo para fora no detalhe; sua planta geral deve ser lida em conjunto com esta ampliação.

ALUNO: Icaro Gamarra Silva

RGM: 3322.527 | CURSO: Engenharia Civil

PROVA DE DESENHO TÉCNICO

PROJETO: 3 LOJAS + 4 APARTAMENTOS

PROFESSORA: Rafaella Scalon

LOCAL: Dourados - MS | Lote hipotético: 20 x 50 m

ENTREGA: 28/10/2026 | REVISÃO: 02

ESTUDO ACADÊMICO / NÃO EXECUTIVO

ESCALAS

1:50 / 1:25


UNIDADES: m / detalhes em cm indicados


07 / 08

A2 / 594 x 420

PROJETO ARQUITETÔNICO • EDIFICAÇÃO DE USO MISTO

VISTAS 3D E SÍNTESE DO PARTIDO

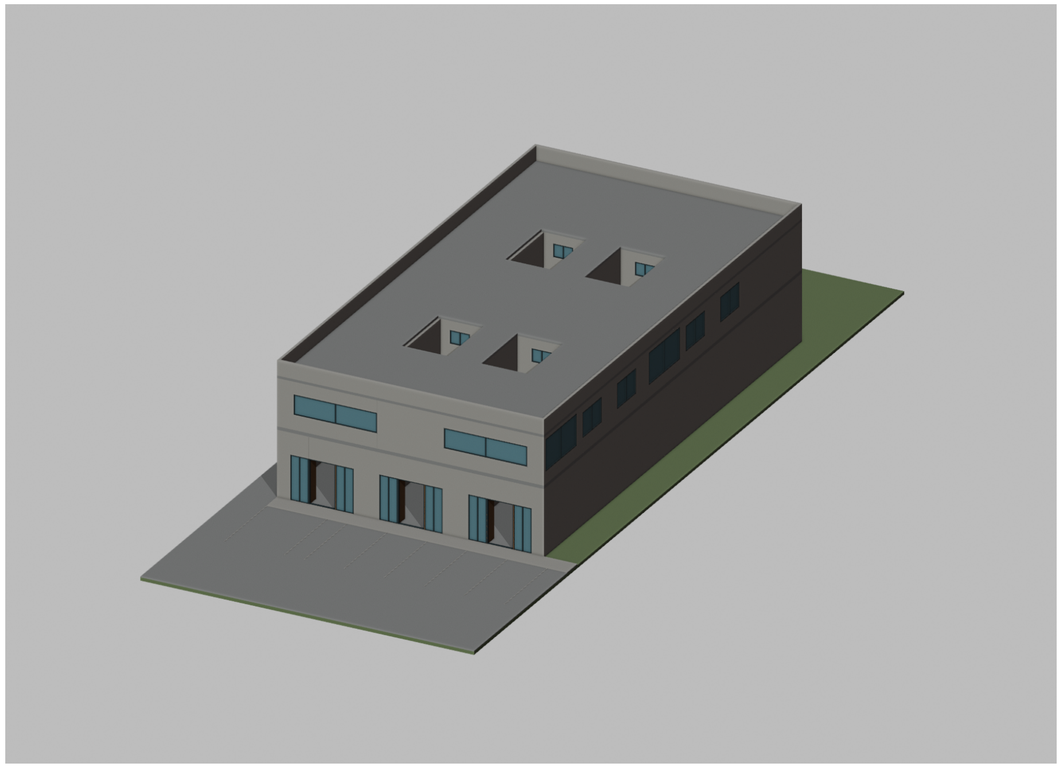

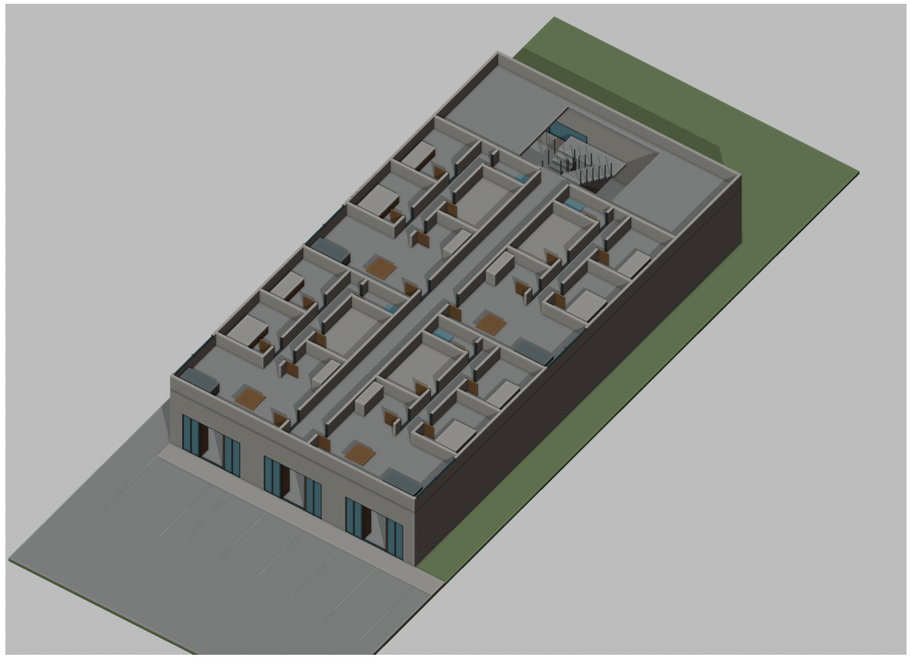

PARTIDO ARQUITETÔNICO

Comércio no térreo e habitação no superior, com acesso residencial separado. Quatro unidades familiares de dois quartos, pátios de iluminação e circulação coletiva posterior. A maquete possui paredes com vãos reais, folhas, caixilhos, vidro, lajes, escada e cobertura com aberturas sobre os pátios.

ARQUIVOS EDITÁVEIS: DXF 2D com layouts A2; DXF 3D de faces; modelo Blender e OBJ. O DXF 3D é malha editável, não sólido paramétrico BIM.

VERIFICAÇÃO LEGAL: lote hipotético sem zona urbanística identificada. Parâmetros municipais e atendimento normativo ainda dependem de consulta e revisão técnica. Este estudo não certifica conformidade nem autoriza execução.

ALUNO: Icaro Gamarra Silva

RGM: 3322.527 | CURSO: Engenharia Civil

PROVA DE DESENHO TÉCNICO

PROJETO: 3 LOJAS + 4 APARTAMENTOS

PROFESSORA: Rafaella Scalon

LOCAL: Dourados - MS | Lote hipotético: 20 x 50 m

ENTREGA: 28/10/2026 | REVISÃO: 02

ESTUDO ACADÊMICO / NÃO EXECUTIVO

ESCALAS

VISTAS SEM ESCALA

UNIDADES: m / detalhes em cm indicados

08 / 08

A2 / 594 x 420